DEPARTEMENT DE LA MANCHE

Communauté d 'Agglomération du COTENTIN

Ville de
CHERBOURG-EN-COTENTIN
(Commune déléguée de TOURLAVILLE)

Pascal SAVELLI
Géomètre
Expert
Foncier

1-3, rue du Général de Gaulle

Propriété de la SARL TEAM-EXPO

Cadastre section 602 AV n° 153

PLAN D'ETAT DES LIEUX ET DE DIVISION VOLUMETRIQUE

Echelle : 1/100

16/02/2026 S.C.P. SAVELLI Pascal , Géomètre Expert Foncier
2, Rue de Becqueret, BP147, 50270 BARNEVILLE-CARTERET - Tel : 02.33.53.86.25
Courriel : scpsavelli@orange.fr

Réf : C 3937

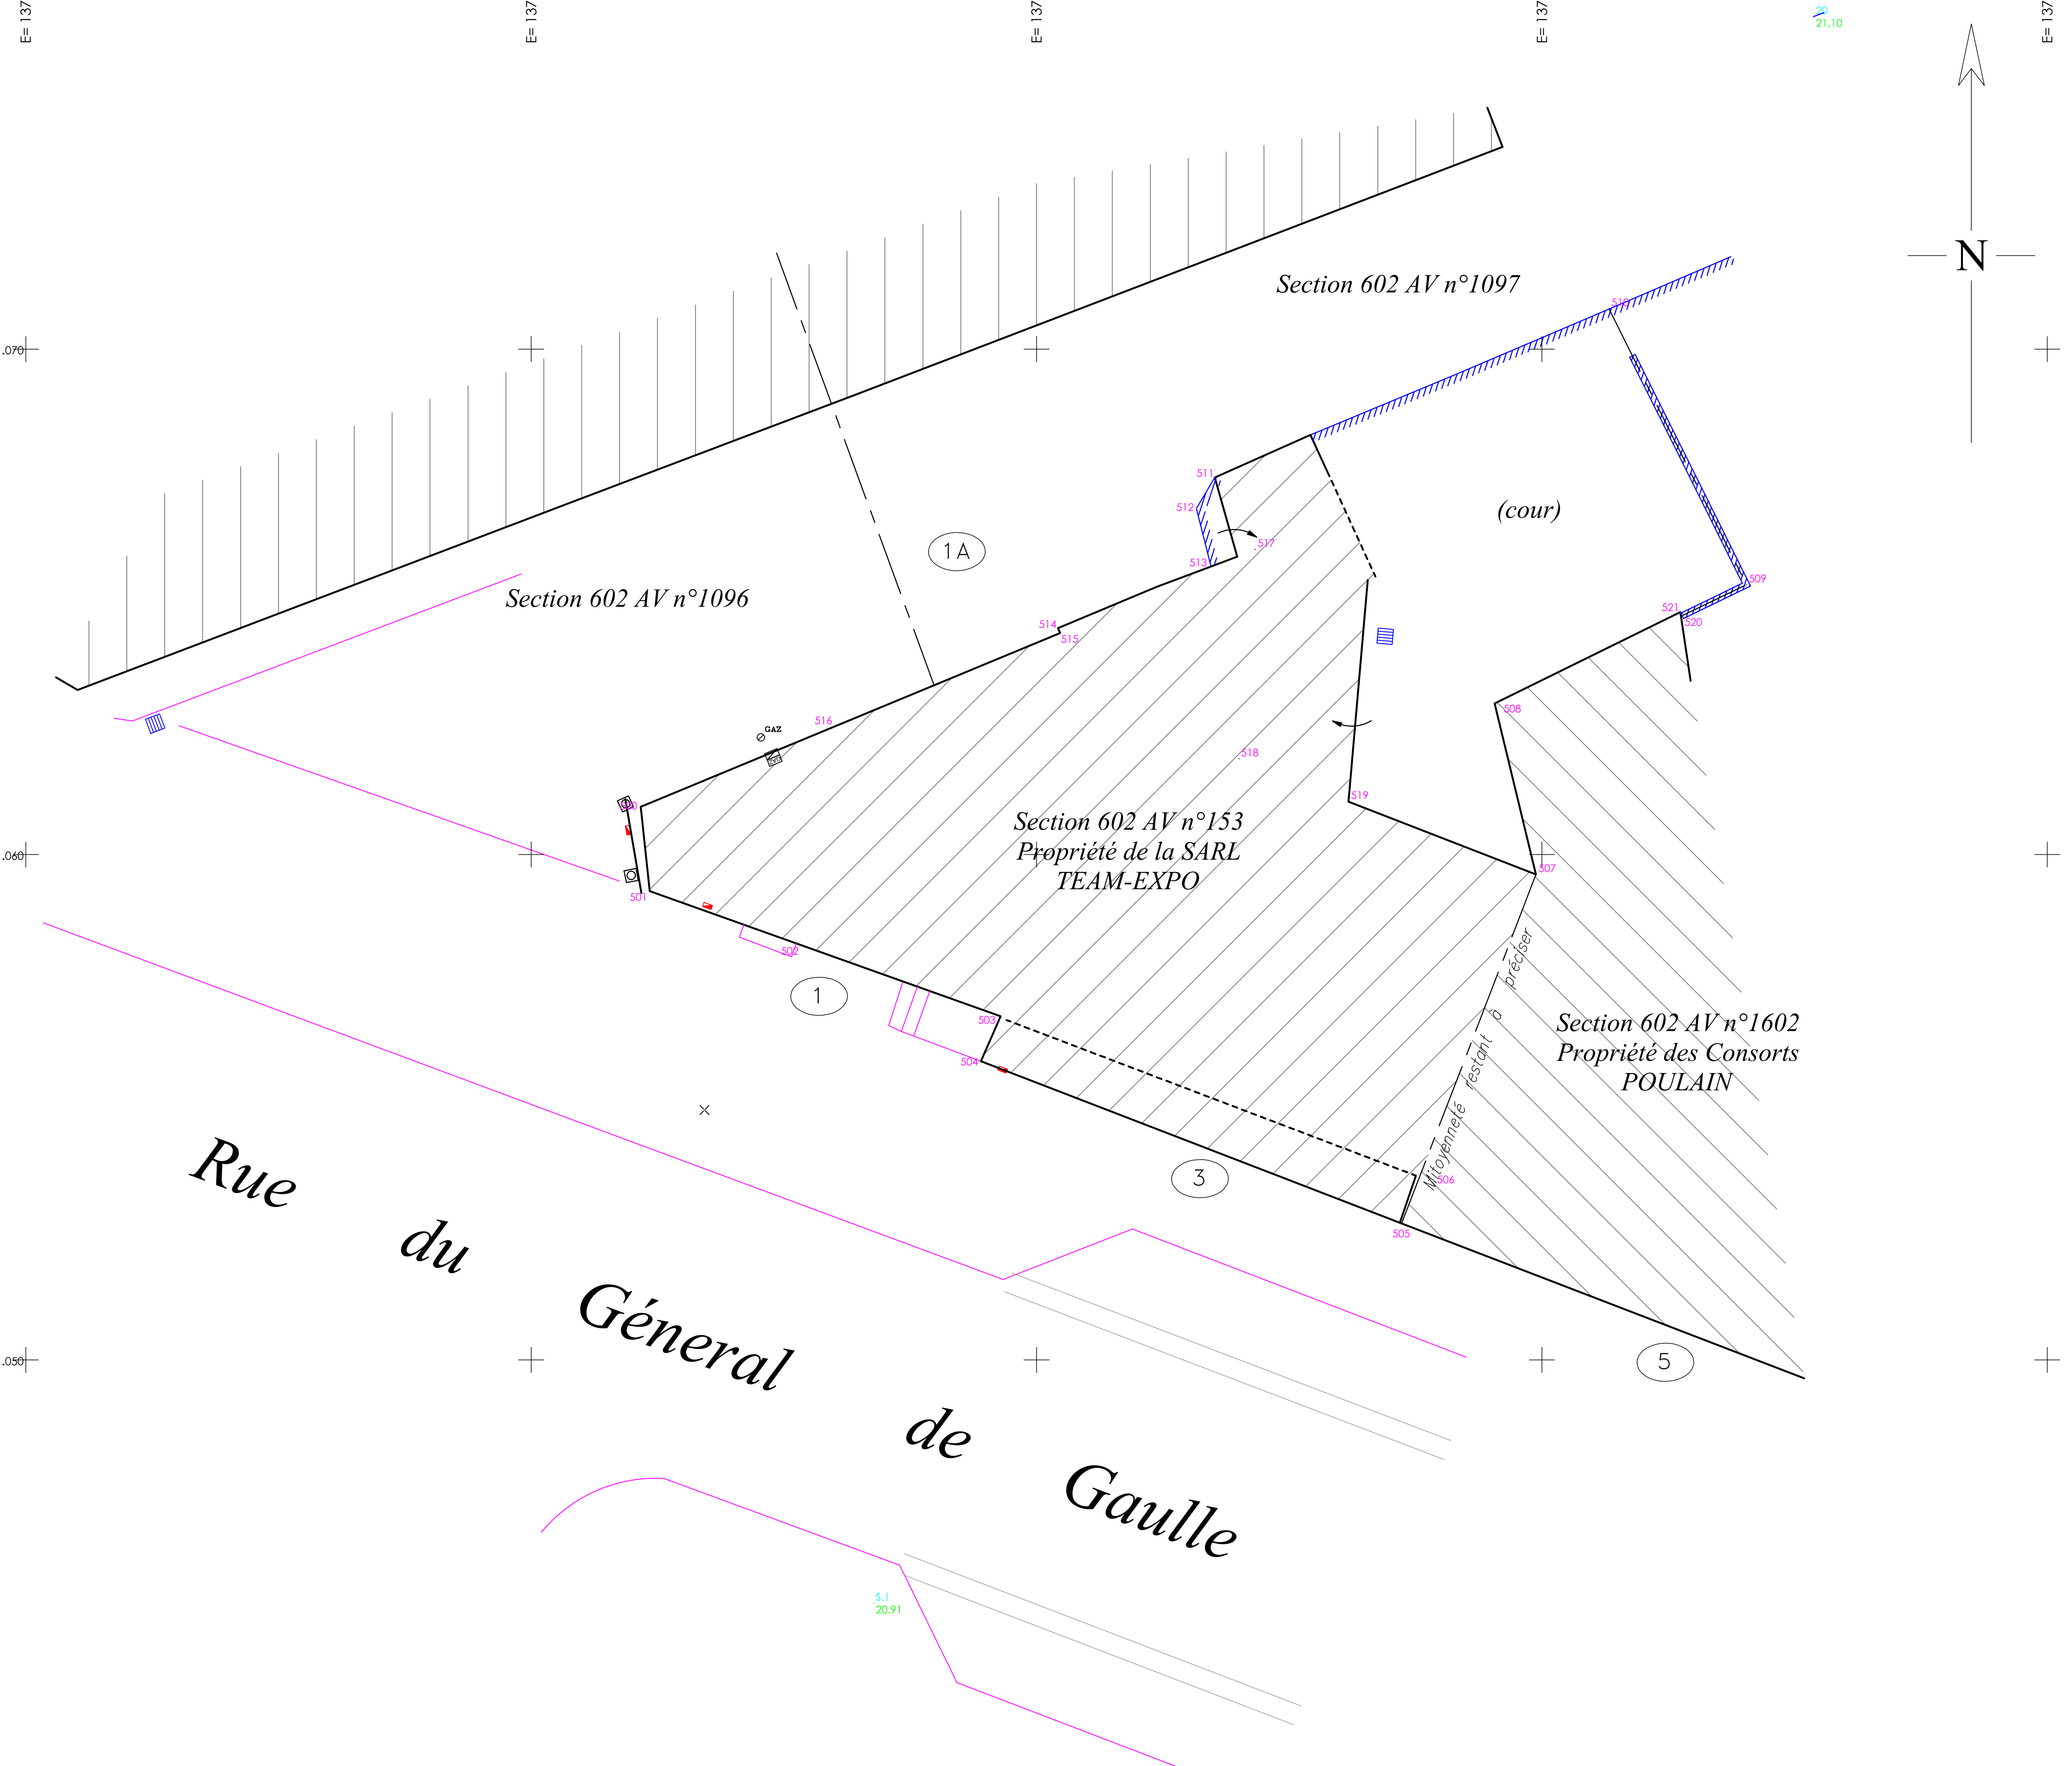

Plan d'état des lieux
échelle 1/100

Echelle : 1/100

Légende

🟩 *Volume n°1*

🟧 *Volume n°2*

RAPPEL DES SERVITUDES A ACTER

- Ⅰ Droit de passage de tuyau d'évacuation d'eaux usées au profit du volume 2 sur le volume 1.
- Ⅱ Droit de vues directes au profit du volume 2 sur le volume 1.
- Ⅲ Droit de tour d'échelle, de débort de toit et de gouttière et de vues directe, au profit du volume 2 sur le volume 1.
- Ⅳ Interdiction par le volume 1 de rehausser le bâtiment arrière situé devant la fenêtre du volume 2.

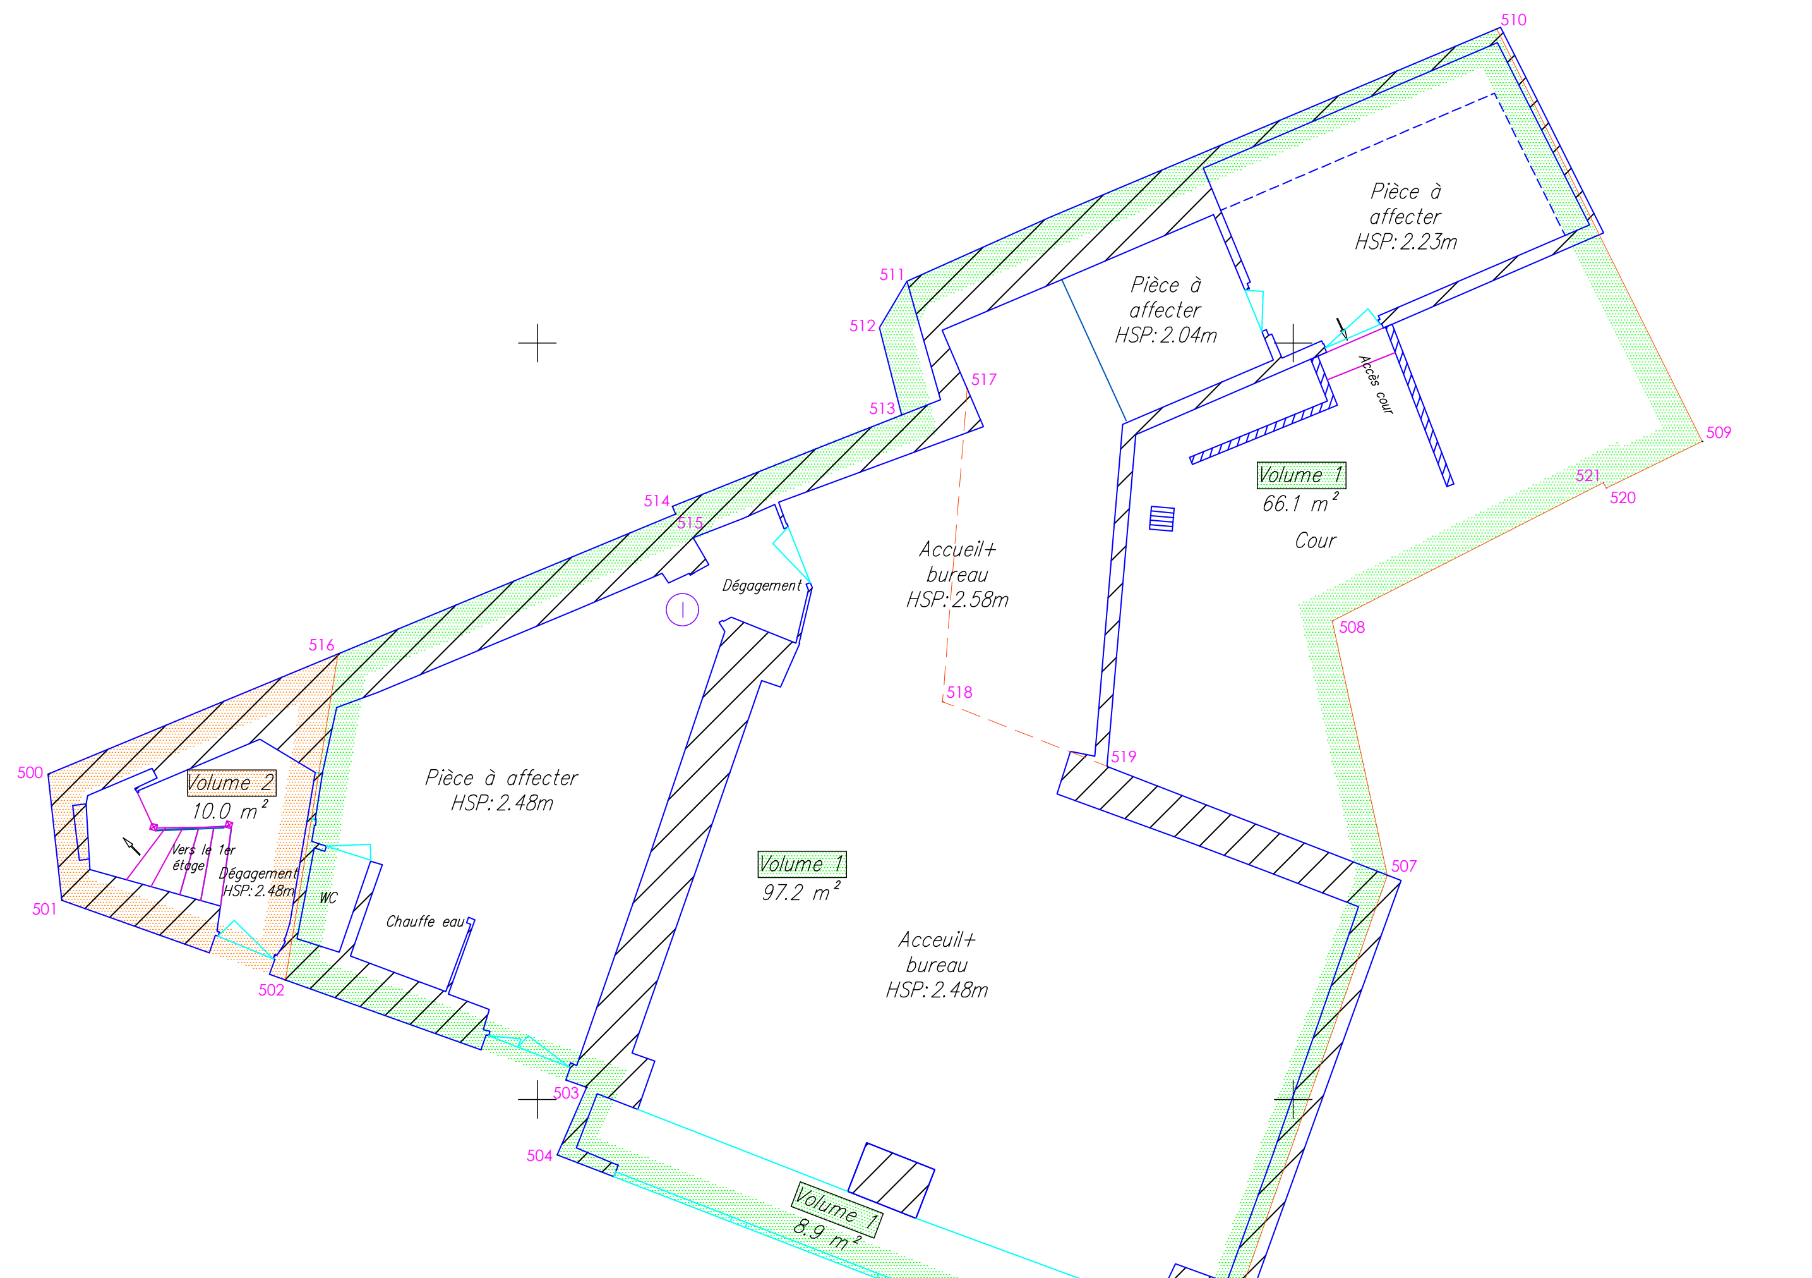

Vue n°1

Rez-de-chaussée: échelle 1/100

Echelle : 1/100

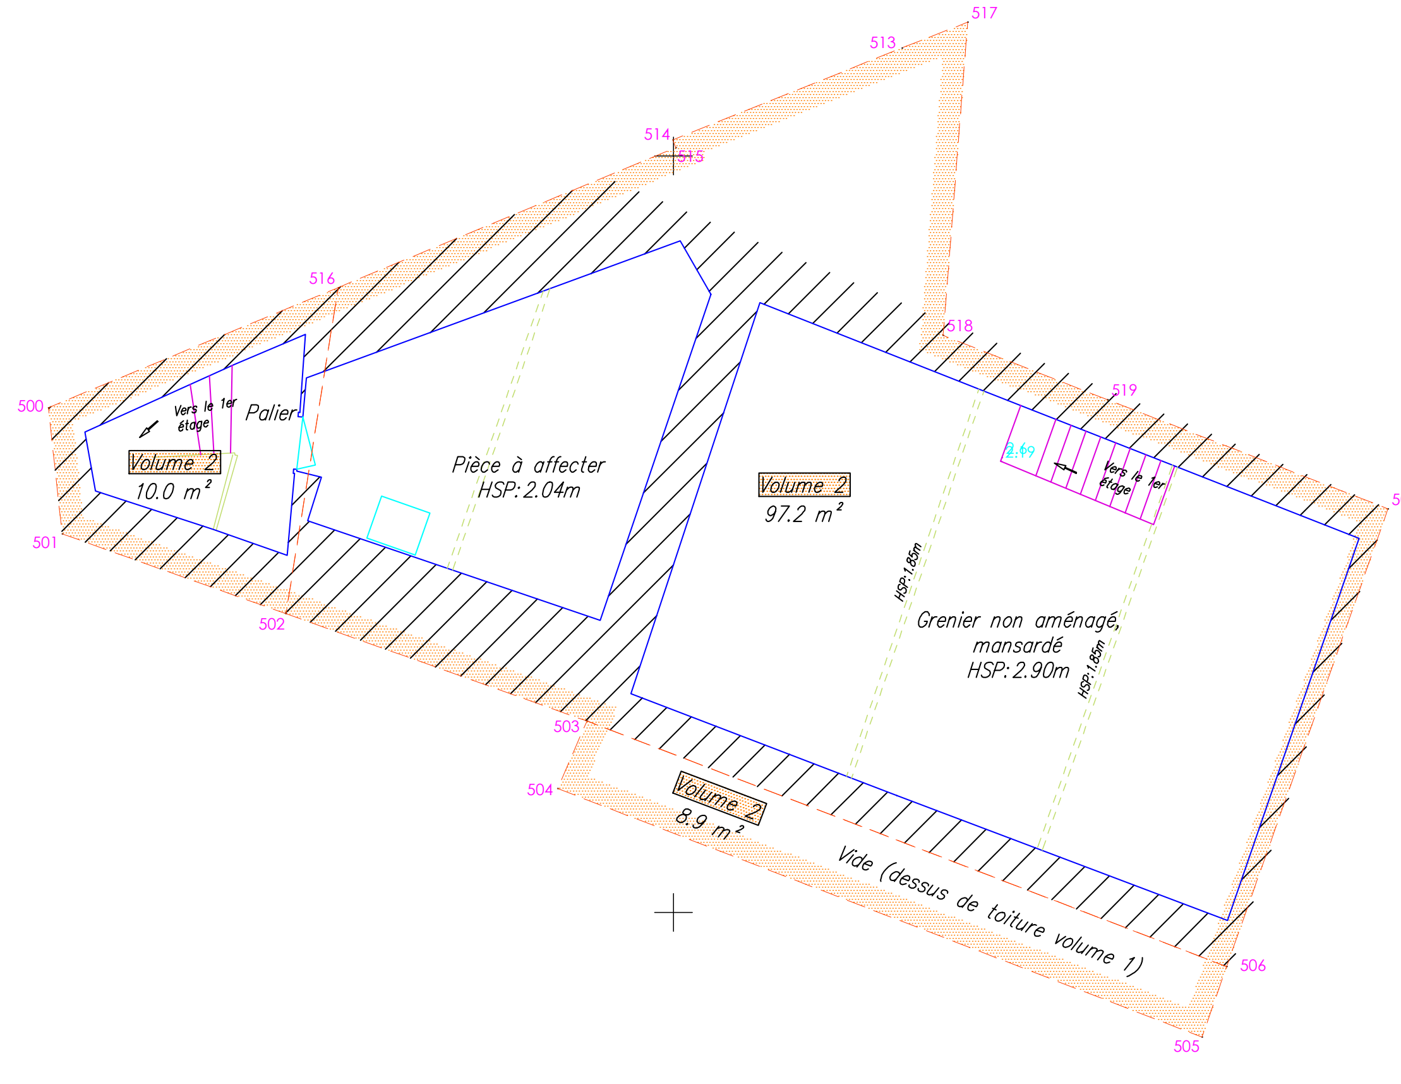

Vue n°3

2ème étage: échelle 1/100

Echelle : 1/100

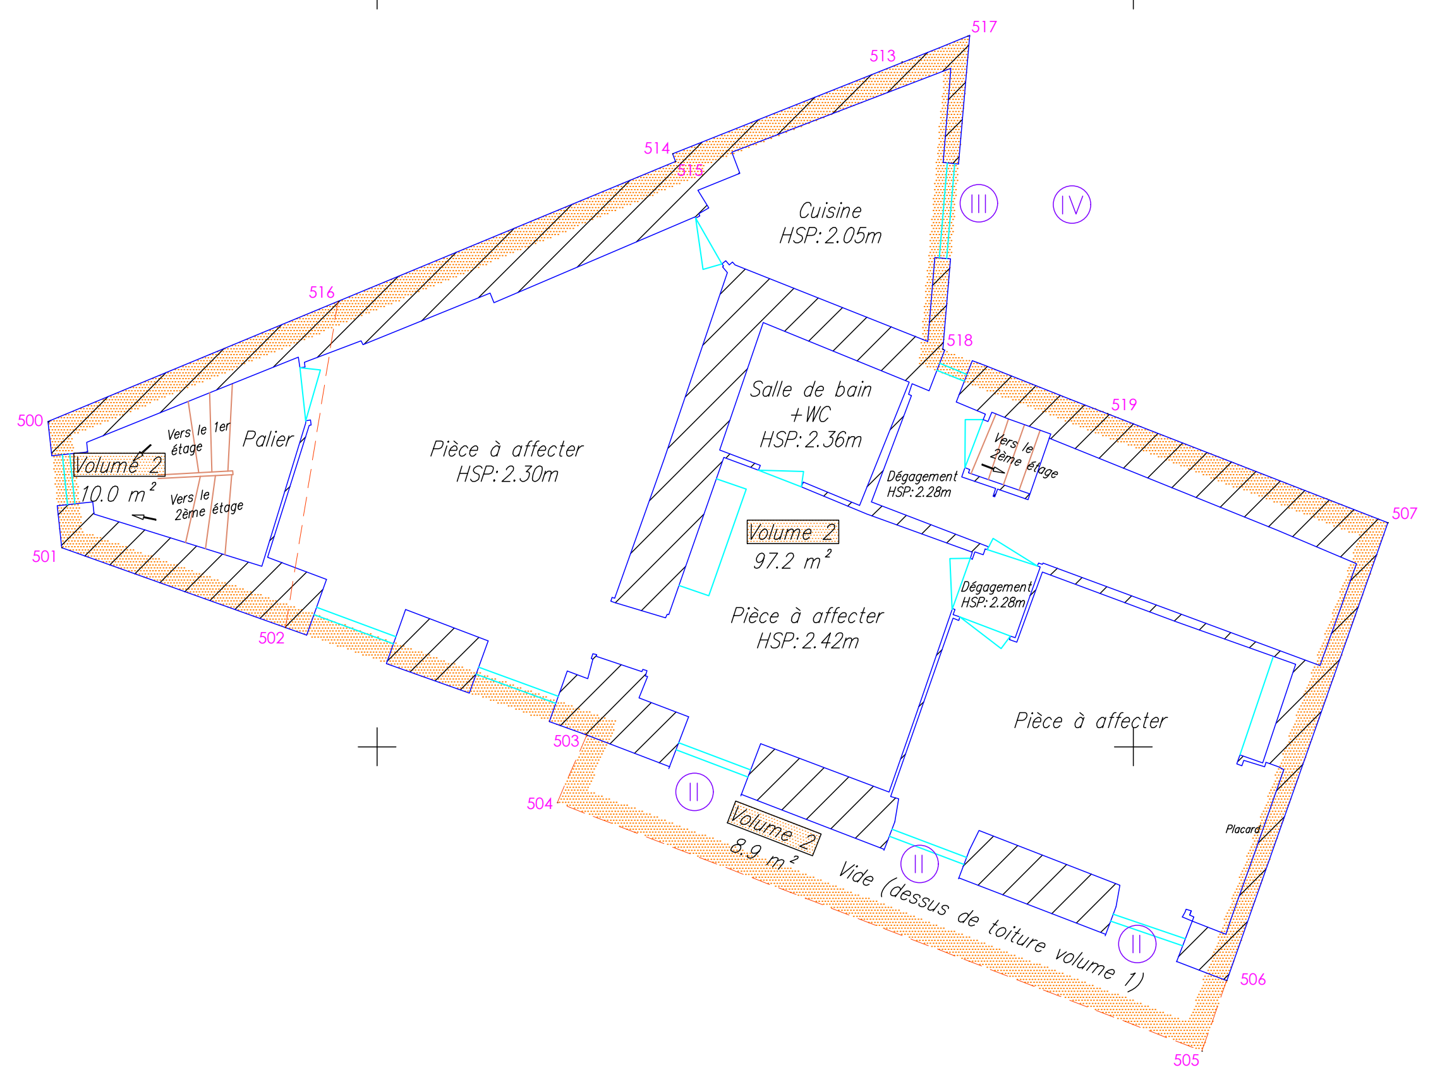

Vue n°2

1er étage: échelle 1/100

Echelle : 1/100

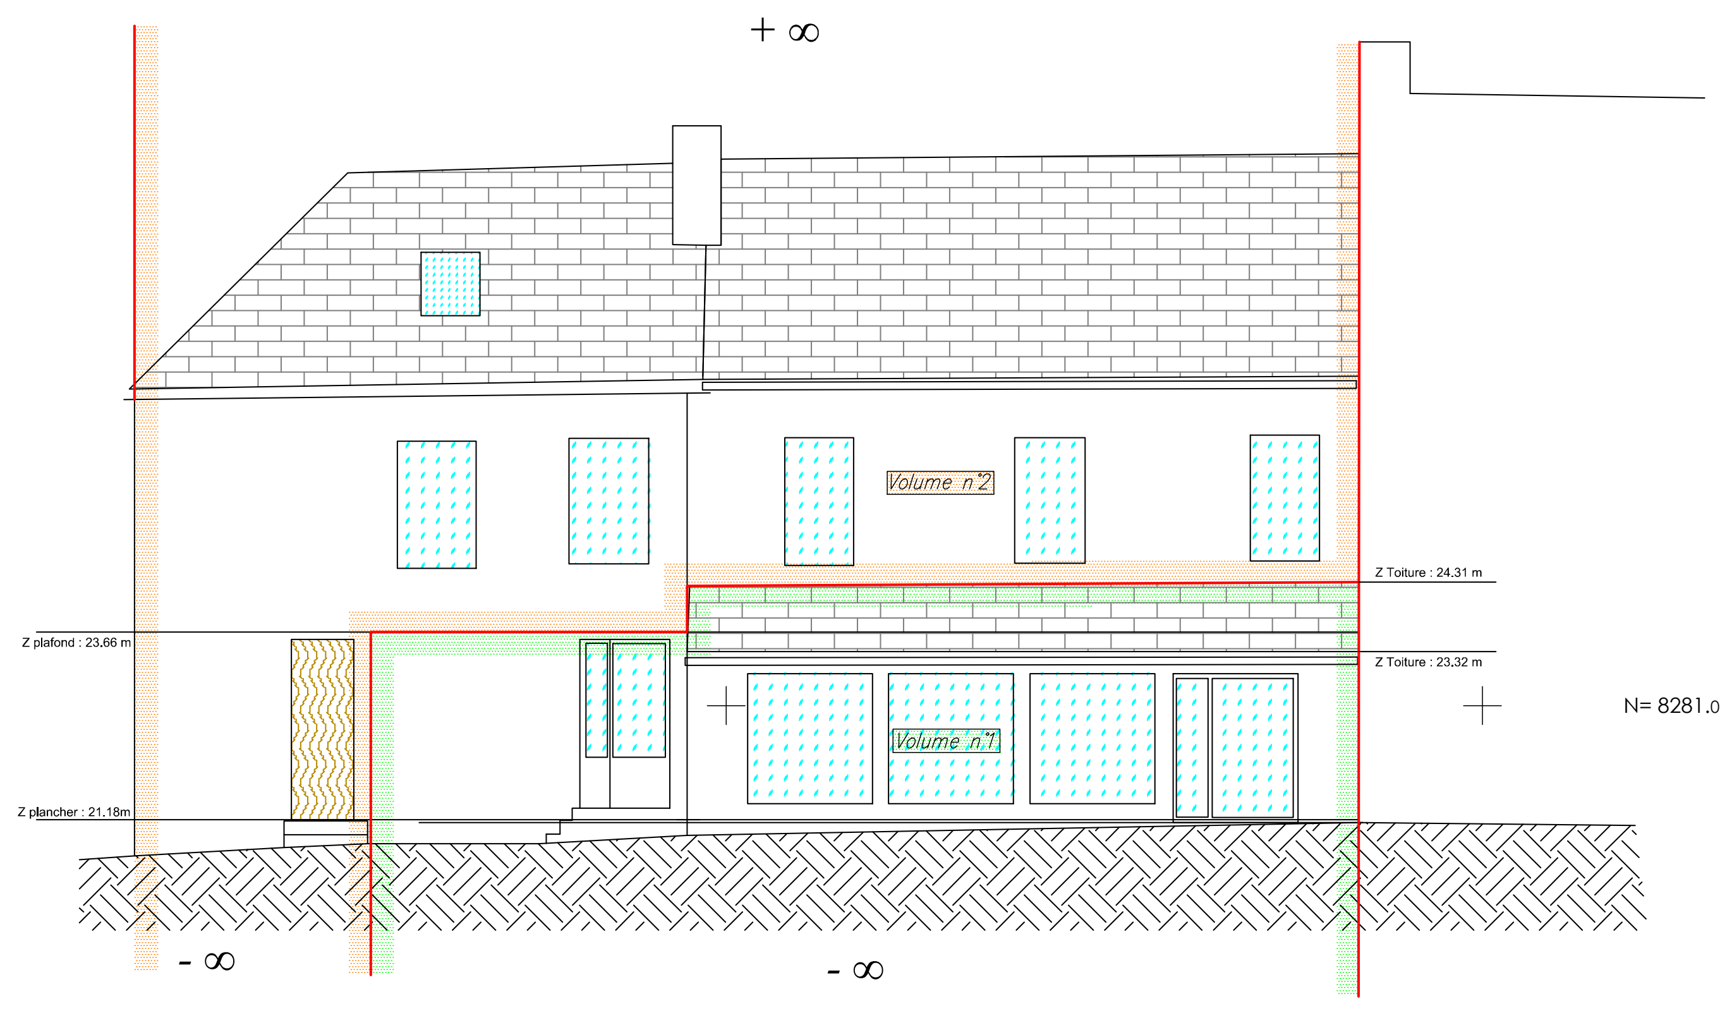

Façade Sud: échelle 1/100

Echelle : 1/100